


1. Дом, 2 этажа: ядро 14×10 м, 2-й этаж 17×10 м (3 м над гаражом)
2. SPA-крыло 8,4×10 м: бассейн 4,0×2,5 м с гидромассажем, сауна, лаунж на 13 мест
3. Гараж 10,4×8,4 м: 2 пикапа класса RAM + мотоцикл + верстак
4. Хозблок и котельная (газ или тепловой насос — без переделки)
5. Терраса 22,4 × 4,5 м + зона BBQ, порог портала 0–20 мм
6. Купель 2×2 м с подогревом и крышкой, в 1 м от выхода из SPA
7. Настольный теннис: зона 7,0×4,3 м
8. Стол на 18–20 мест под биоклиматической перголой
9. BBQ-блок: мангал, казан, мойка, столешница, шкафы
10. Въезд №1: откатные ворота 9,2 м прямо перед гаражом
11. Въезд №2: распашные ворота 4,1 м, за ними свободная манёвровая зона
12. Гостевая парковка 5 мест 2,7×5,5 м на газонной решётке
13. Моечная точка: катушки ВД и воды, пылесос, химия, лоток с маслоуловителем
14. Баскетбол: штрафная 4,6 м, дуга 6,75 м, сетка-ловушка за щитом
15. Вольер 3,1×7,0 м, будка в стене хозблока, калитка на участок
16. Собачий туалет: моющееся покрытие, трап, кран
17. Колодец (существующий) — обследовать: дебит, анализ
18. Калитка к родителям: доводчик, замок на высоте 1,5 м
19. Детская зона: батут Ø4,3 м, башня с горкой
20. Воркаут вдоль SPA: рукоход, кольца, канат, турник, брусья
21. Газон: бадминтон 13,4×5,2 м, волейбол на съёмных стойках
22. Костровая Ø4,4 м на 10–12 мест, газовый очаг
23. Взрослые качели
24. ≈40 туй вдоль нижней границы — сохраняются, защита на время стройки
25. Шаровидные туи (6 шт.) — по дендроплану, к лестницам террасы
26. Розарий — по дендроплану, бордюр перед террасой
27. Колоновидные яблони и груша — экран между садом и парковкой
28. Ягодник и резерв под 2 грядки
29. ЛОС, подъезд ассенизатора через въезд №2
30. Главный вход с навесом со стороны парковки
31. Техдвор кондиционеров за SPA, за шумозащитным экраном из ламелей
32. Курительная точка под навесом у выхода из SPA
33. Резерв: скважина — только если колодец не пройдёт проверку
34. Тандыр на негорючей площадке 1,4×1,4 м, 5,3 м от стены дома
35. Детские качели (2 места) у SPA; домик на дереве — если дерево подойдёт
36. Наружный хозвход в цоколь: приямок с лестницей у гаража
37. Площадка под наружный блок теплового насоса (резерв)
38. Гильзы в грунте под стойки сетки бадминтона и волейбола
39. Забор-«шлюз»: площадка въезда №1 отделена от участка — собака не выбежит


ГП-1	**Генеральный план участка** Масштаб — по линейке 0–5–10 м · верх листа = северо-восток (35°) · пунктир — траектории пикапа	Жилой дом с SPA и гаражом · ред. П1.2 · д. Тверитино КН 50:32:0030118:1930 · 1 200 м²	Стадия: концепция П0 07.10.2026

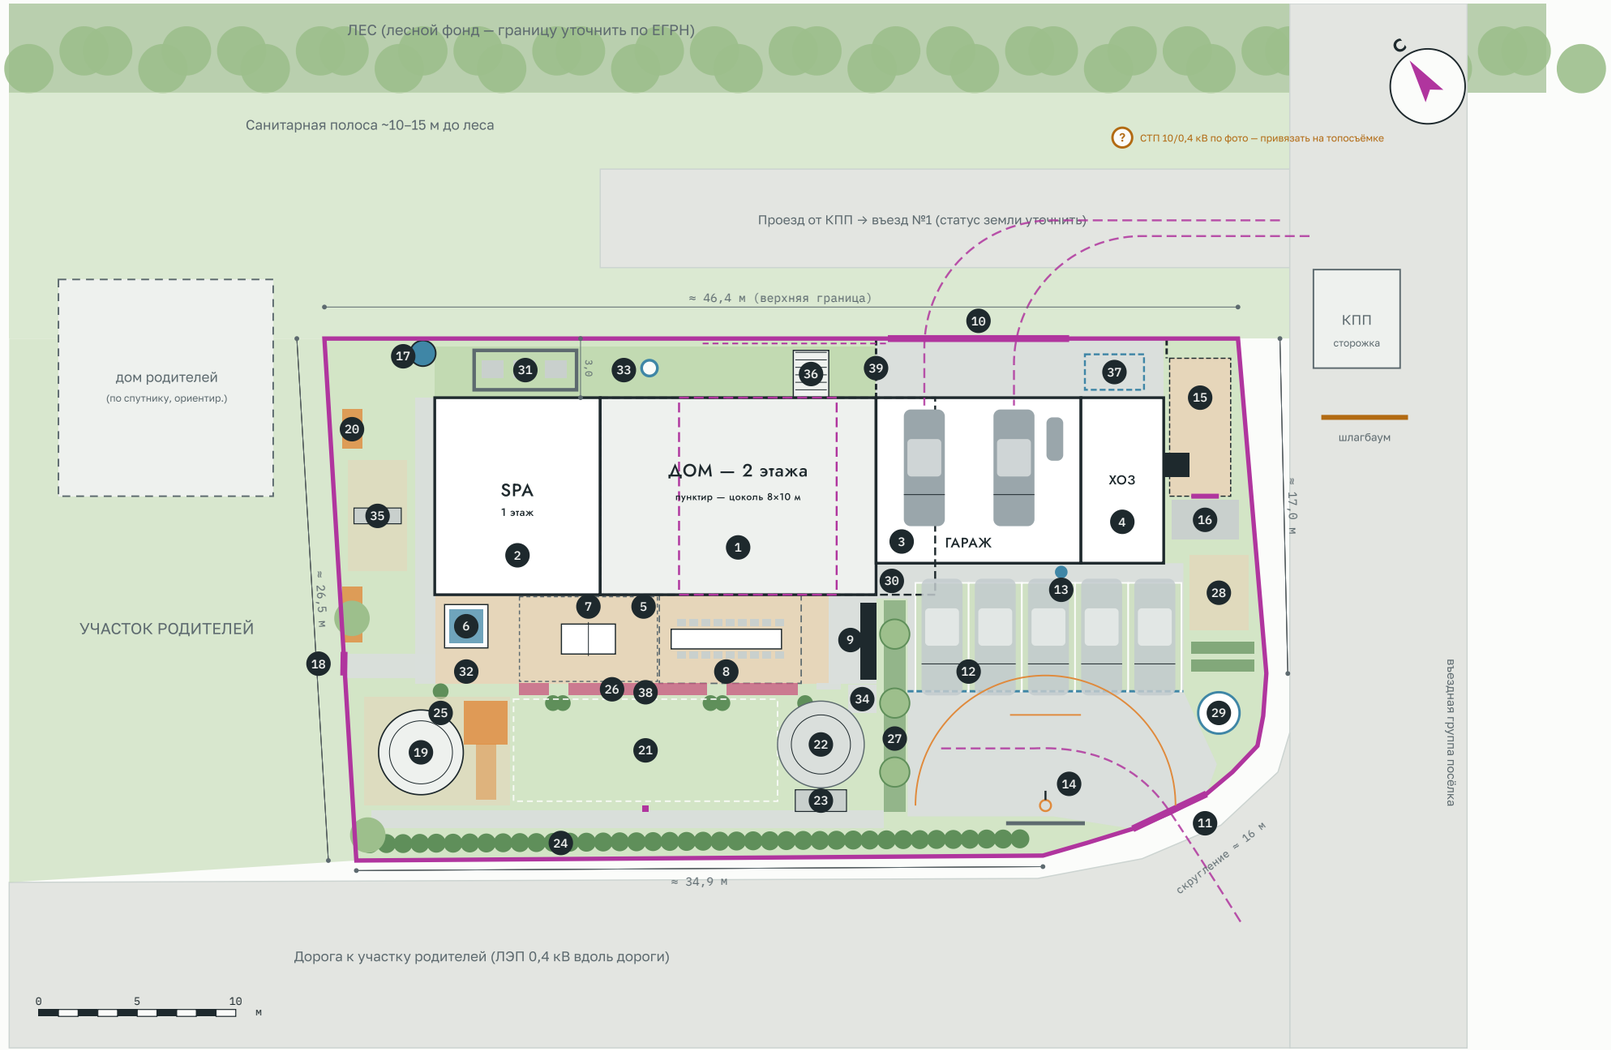

1.01 Зал бассейна + лаунж SPA 51,0
1.02 Раздевалка SPA (вход из дома) 6,6
1.03 С/у SPA: WC, душ, раковина 5,1
1.04 Сауна 4–5 чел. 6,8
1.05 Кухня-гостиная 62,6
1.06 Лестница (с маршем в цоколь) 10,5
1.07 Холл 8,6
1.08 Хозяйственная кладовая 7,1
1.09 Гостевая спальня 15,0
1.10 Душ / WC гостевой 4,3
1.11 Тамбур-прихожая 11,0
1.12 Гараж 2 авто + мото 73,0
1.13 Котельная / теплоузел 9,4
1.14 Хозблок 19,7

АР-1	**План 1 этажа** Потолки: жилые 3,0 м · SPA 3,2 м · гараж 3,2 м	Жилой дом с SPA и гаражом · ред. П1.2 · д. Тверитино КН 50:32:0030118:1930 · 1 200 м²	Стадия: концепция П0 07.10.2026


17,0 (над гаражом 3,0 м)

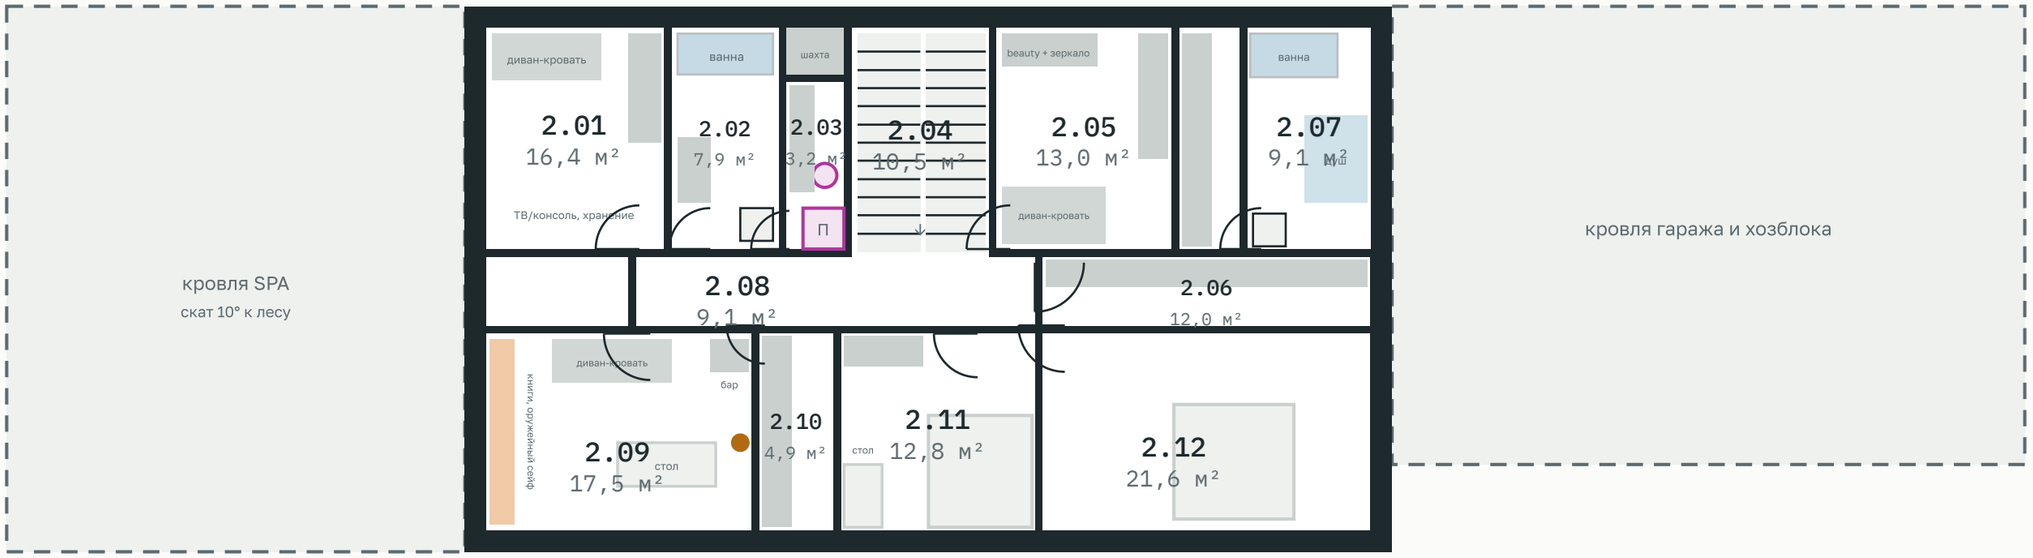

2.01 Игровая 16,4
2.02 Семейный санузел (ванна) 7,9
2.03 Бельевой узел: бельепровод, подъёмник 3,2
2.04 Лестница 10,5
2.05 Комната Насти 13,0
2.06 Мастер-гардеробная 12,0
2.07 Мастер-санузел 9,1
2.08 Коридор 9,1
2.09 Кабинет 17,5
2.10 Кладовая-буфер 4,9
2.11 Спальня Максима 12,8
2.12 Мастер-спальня 21,6


АР-2	**План 2 этажа** Потолки 2,8 м · коридор 2,5 м под воздуховоды	Жилой дом с SPA и гаражом · ред. П1.2 · д. Тверитино КН 50:32:0030118:1930 · 1 200 м²	Стадия: концепция П0 07.10.2026

8,0 × 10,0 — под лестницей, холлом и кладовой

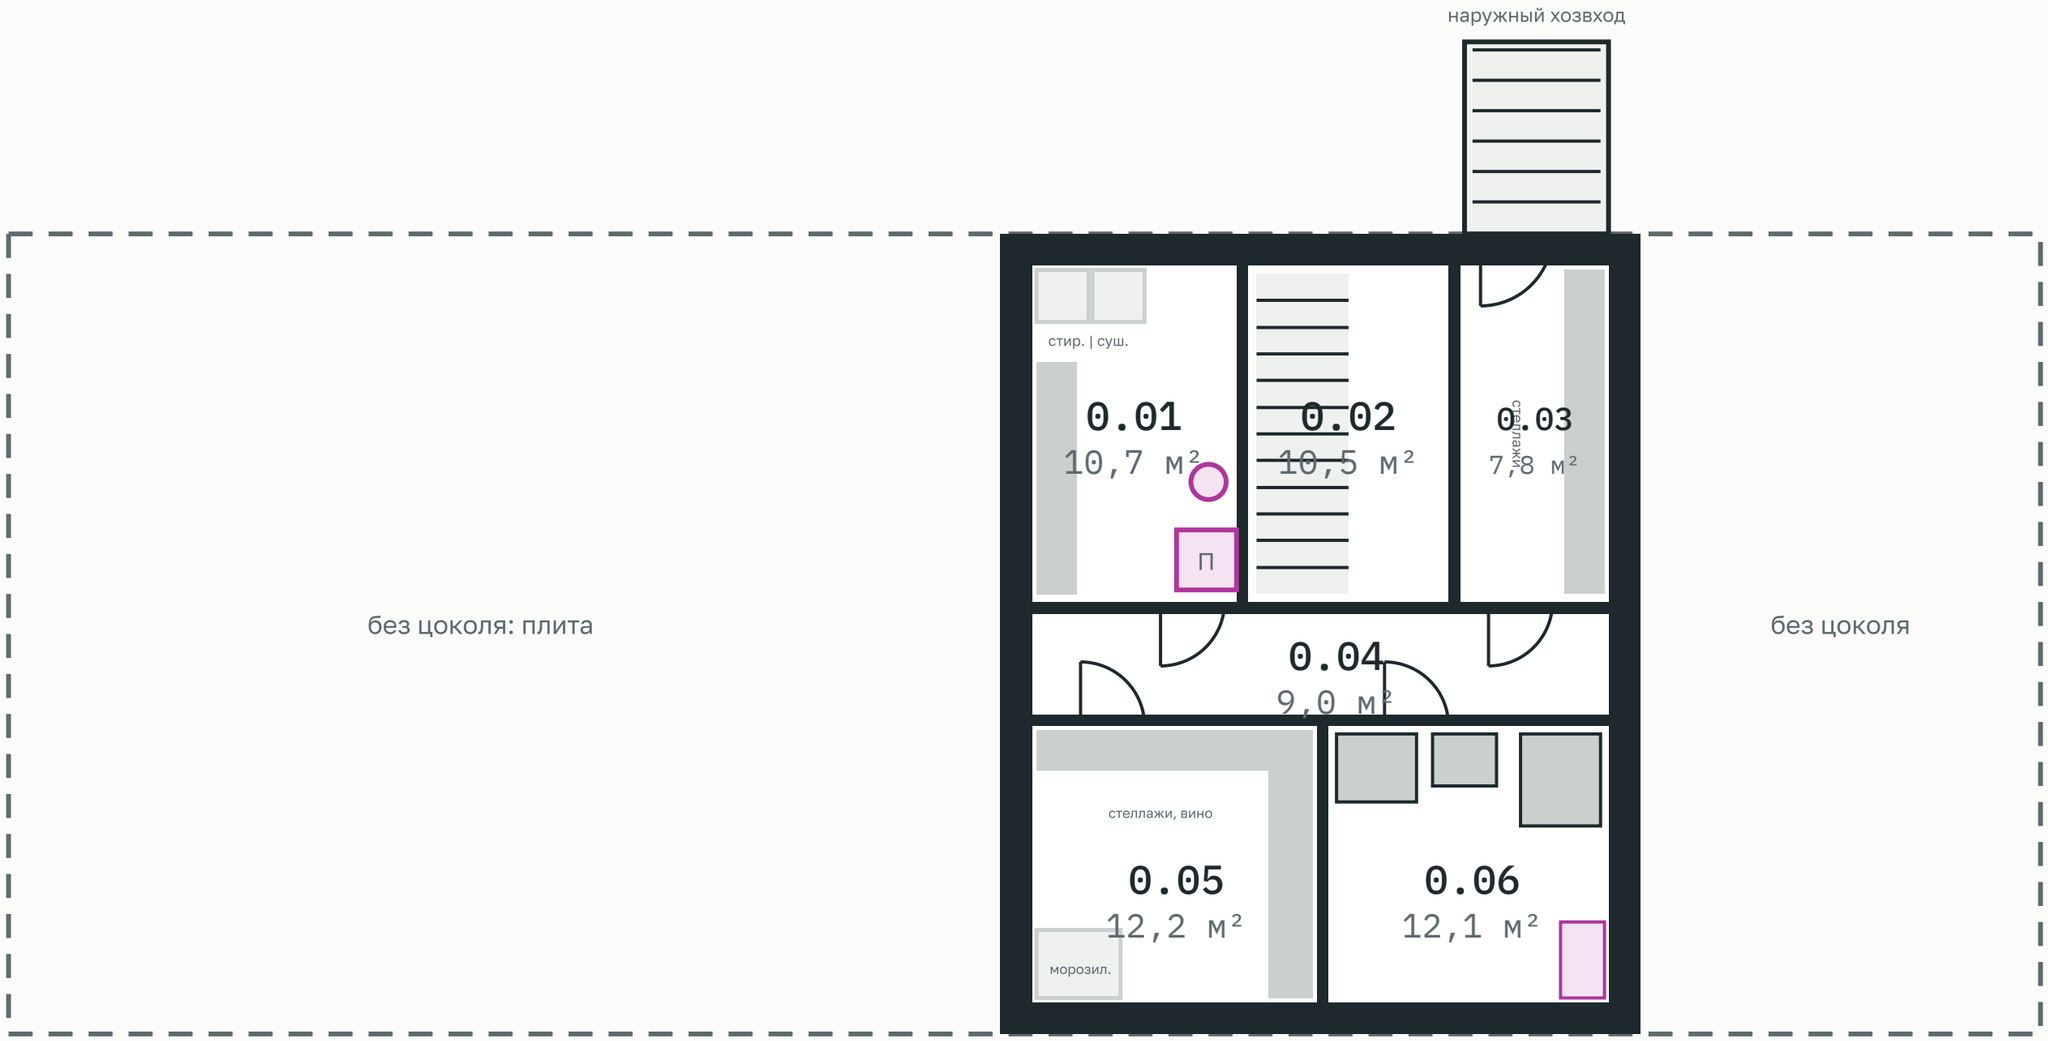


0.01 Постирочная 10,7
0.02 Лестница 10,5
0.03 Хозвход с улицы + сезонное хранение 7,8
0.04 Лобби цоколя 9,0
0.05 Прохладная кладовая: продукты, морозильник, напитки 12,2
0.06 Техпомещение: вода, бассейн, электрика 12,1

АР-0	**План цоколя** 70 м² — только под хозяйственной вертикалью	Жилой дом с SPA и гаражом · ред. П1.2 · д. Тверитино КН 50:32:0030118:1930 · 1 200 м²	Стадия: концепция П0 07.10.2026

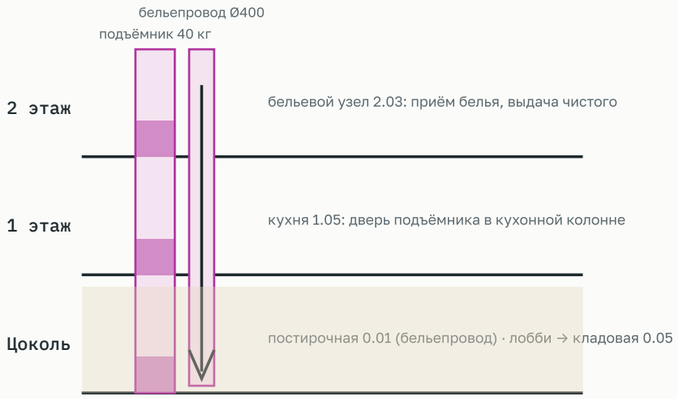



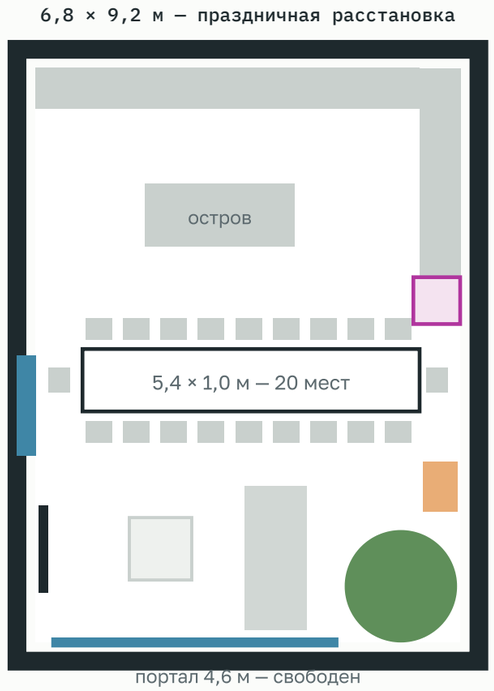

Подъёмник 40 кг: цоколь — кухня — бельевой узел. Бельепровод Ø400 в постирочную. Маршрут из гаража в кладовую ≈10 м под крышей. Стол 5,4×1,0 м на 20 мест без перестановки дивана, ёлки и аквариума.

АР-5	**Хозвертикаль, маршрут, стол на 20** Схемы к ТЗ на корректировку, п. 35	Жилой дом с SPA и гаражом · ред. П1.2 · д. Тверитино КН 50:32:0030118:1930 · 1 200 м²	Стадия: концепция П0 07.10.2026